
PEDRINHAS · CASA DO ÁTRIO SOCIAL · PROJETO 04

PLANTA HUMANIZADA · TÉRREO

Estudo arquitetônico R1 · 13/11/2026 · dimensões em metros

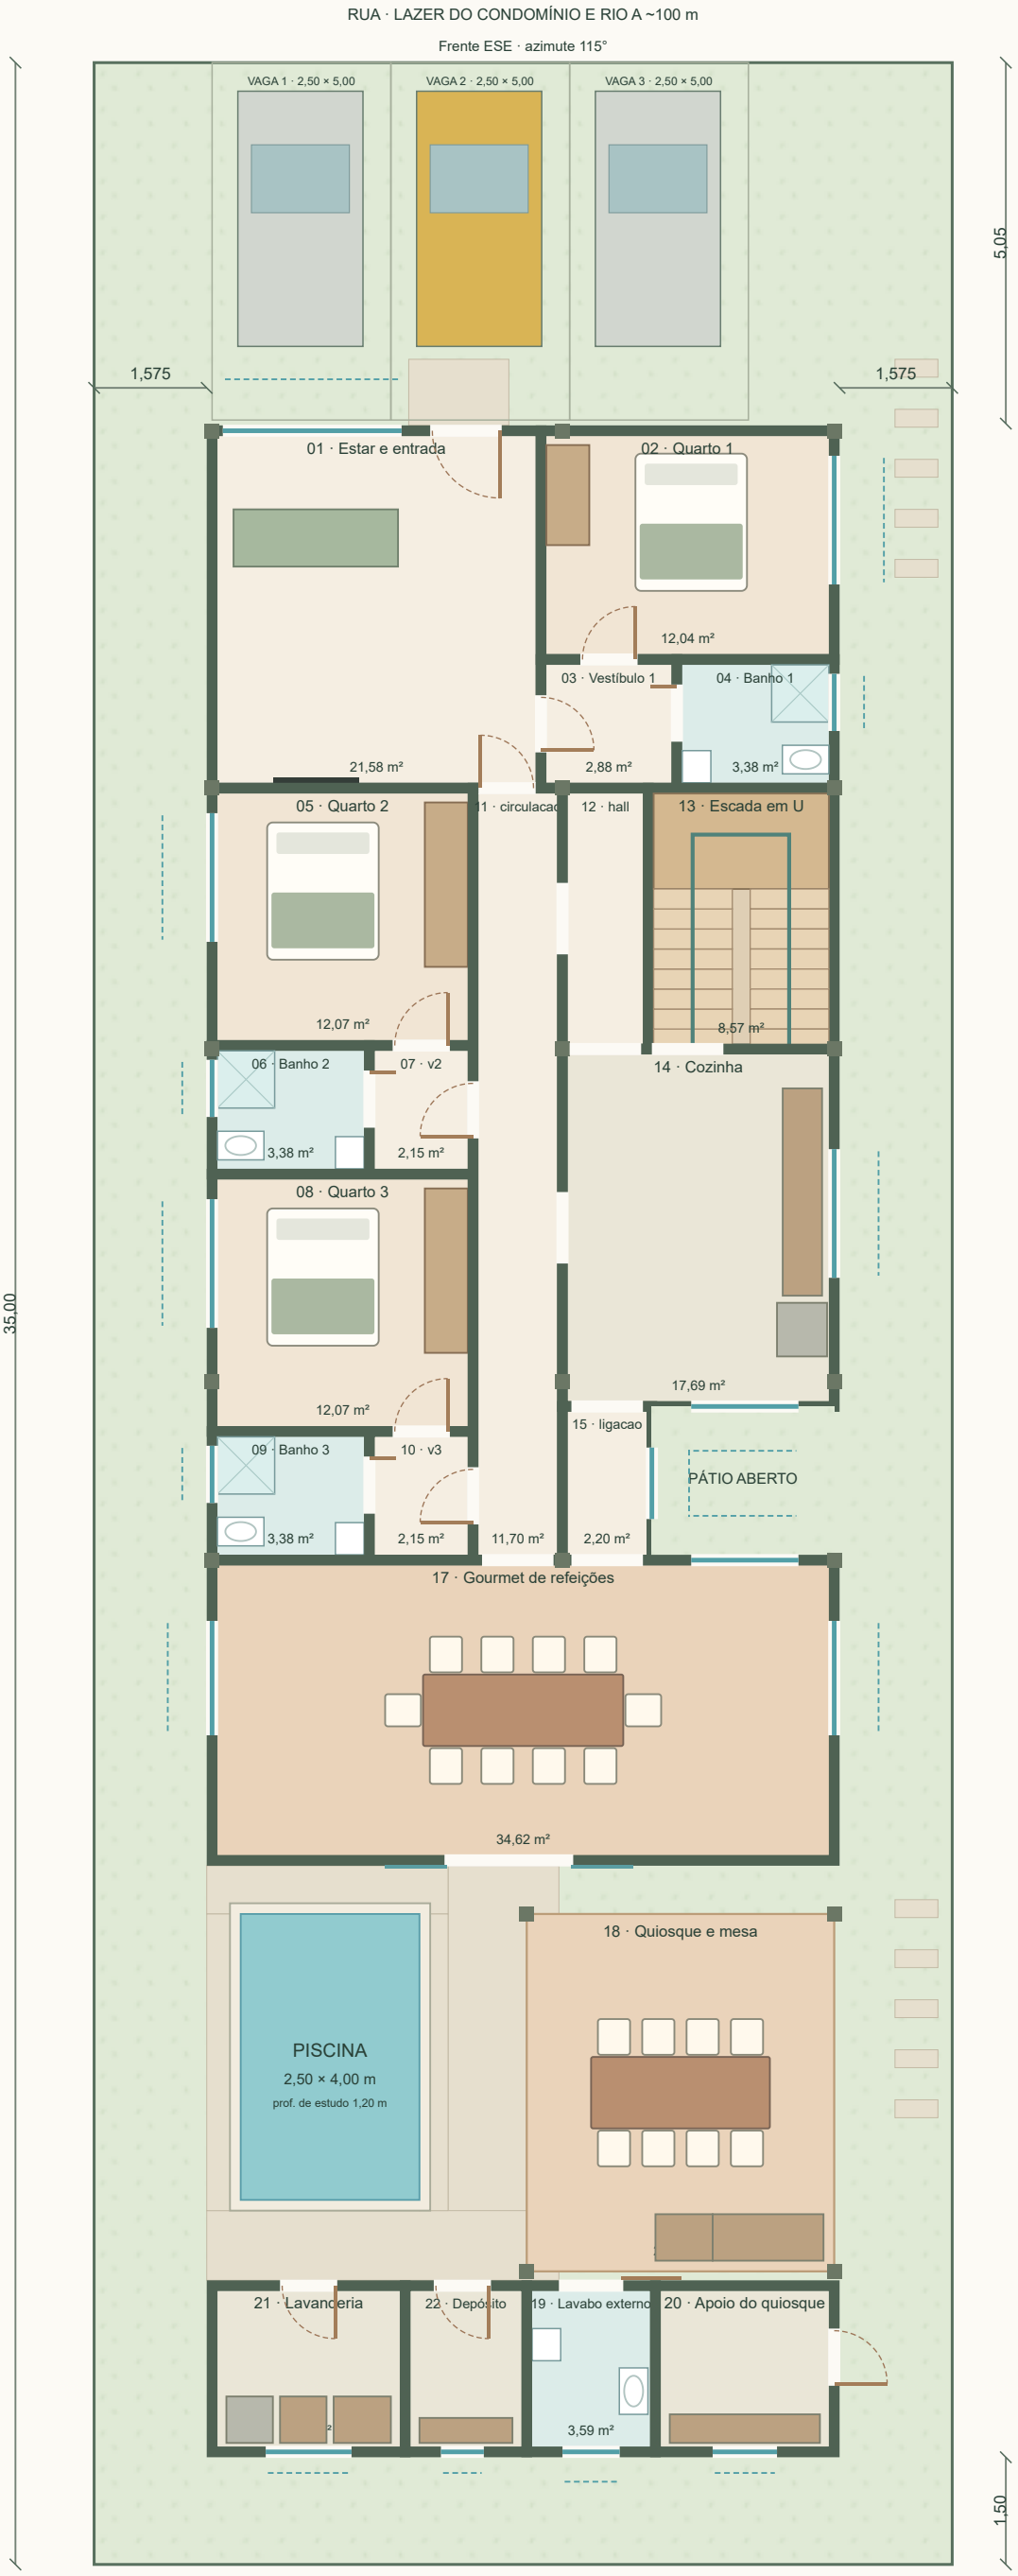

AMBIENTES · ÁREA ÚTIL ESTIMADA

01 Estar e entrada
4,45 × 4,85 · 21,58 m²

02 Quarto 1
3,95 × 3,05 · 12,04 m²

03 Vestíbulo 1
1,75 × 1,65 · 2,88 m²

04 Banho 1
2,05 × 1,65 · 3,38 m²

05 Quarto 2
3,50 × 3,45 · 12,07 m²

06 Banho 2
2,05 × 1,65 · 3,38 m²

07 Vestíbulo 2
1,30 × 1,65 · 2,15 m²

08 Quarto 3
3,50 × 3,45 · 12,07 m²

09 Banho 3
2,05 × 1,65 · 3,38 m²

10 Vestíbulo 3
1,30 × 1,65 · 2,15 m²

11 Circulação
1,10 × 10,65 · 11,70 m²

12 Hall da escada
1,05 × 3,50 · 3,67 m²

13 Escada em U
2,45 × 3,50 · 8,57 m²

14 Cozinha
3,65 × 4,85 · 17,69 m²

15 Ligação coberta ao gourmet
1,10 × 2,00 · 2,20 m²

16 Pátio-jardim aberto
5,48 m² abertos

17 Gourmet de refeições
8,55 × 4,05 · 34,62 m²

18 Quiosque e mesa
4,15 × 4,85 · 21,46 m²

19 Lavabo externo
1,65 × 2,18 · 3,59 m²

20 Apoio do quiosque
2,35 × 2,18 · 5,11 m²

21 Lavanderia
2,55 × 2,18 · 5,55 m²

22 Depósito
1,55 × 2,18 · 3,37 m²

5 quartos · 3 banhos reversíveis + 2 privativos

Janelas propostas abrindo para fora

Gourmet: 10 lugares · quiosque: 8 lugares

Escada: 18 espelhos de 17,5 cm; piso 28 cm


Guarda-corpos: 1,10 m no desenho

Vigas e pilares: reserva arquitetônica, sem cálculo

Acesso lateral em gramado: rota secundária

Entrada principal e percurso interno: piso contínuo

ORIENTAÇÃO E VENTO · dados do briefing

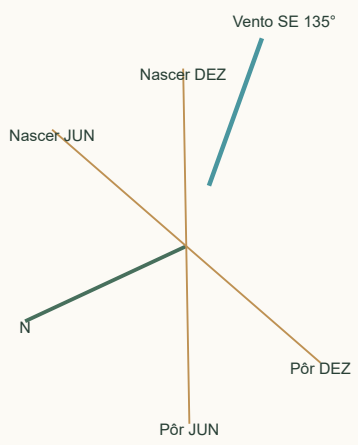

ESCALA GRÁFICA · metros



1:100 ao imprimir em A3, sem ajustar à folha.

Solo natural conservador: 127,23 m² (30,29%)

Inclui exclusão de vagas, piscina, pisos e beirais.


Estudo para avaliação. Executivo e licenças posteriores.

Cotas gerais nas faces externas; dimensões úteis estimadas no quadro.

PEDRINHAS · CASA DO ÁTRIO SOCIAL · PROJETO 04

PLANTA HUMANIZADA · PAVIMENTO SUPERIOR

Estudo arquitetônico R1 · 13/11/2026 · dimensões em metros

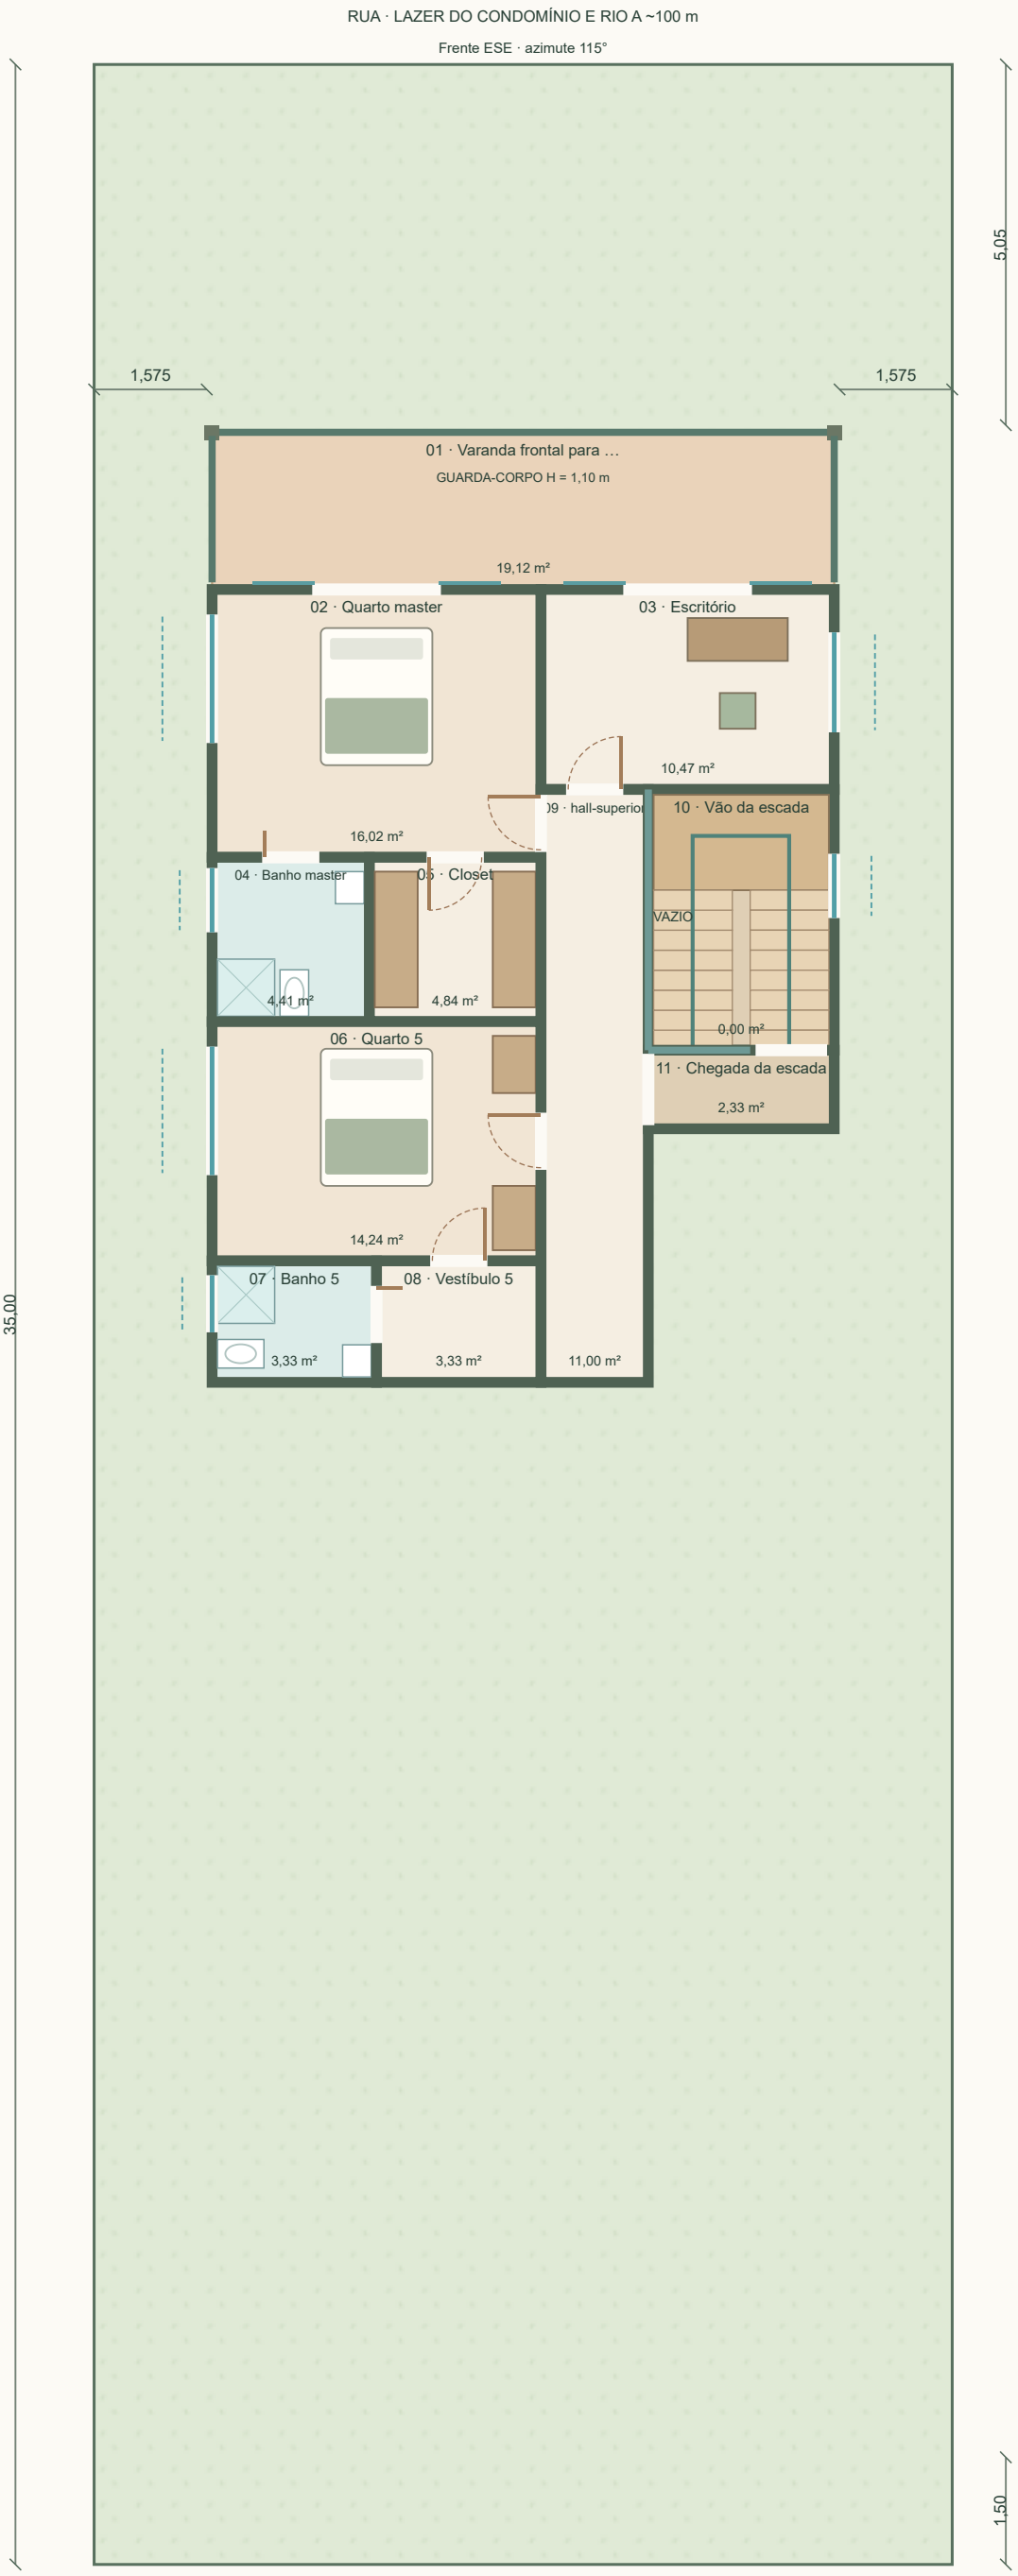

AMBIENTES · ÁREA ÚTIL ESTIMADA

01 Varanda frontal para o rio
8,55 × 2,05 · 19,12 m²

02 Quarto master
4,45 × 3,60 · 16,02 m²

03 Escritório
3,95 × 2,65 · 10,47 m²

04 Banho master
2,05 × 2,15 · 4,41 m²

05 Closet
2,25 × 2,15 · 4,84 m²

06 Quarto 5
4,45 × 3,20 · 14,24 m²

07 Banho 5
2,15 × 1,55 · 3,33 m²

08 Vestíbulo 5
2,15 × 1,55 · 3,33 m²

09 Circulação superior
1,35 × 8,15 · 11,00 m²

10 Vão da escada
2,45 × 3,50 · 0,00 m²

11 Chegada da escada
2,45 × 0,95 · 2,33 m²

5 quartos · 3 banhos reversíveis + 2 privativos

Janelas propostas abrindo para fora

Gourmet: 10 lugares · quiosque: 8 lugares

Escada: 18 espelhos de 17,5 cm; piso 28 cm


Guarda-corpos: 1,10 m no desenho

Vigas e pilares: reserva arquitetônica, sem cálculo

Acesso lateral em gramado: rota secundária

Entrada principal e percurso interno: piso contínuo

ORIENTAÇÃO E VENTO · dados do briefing

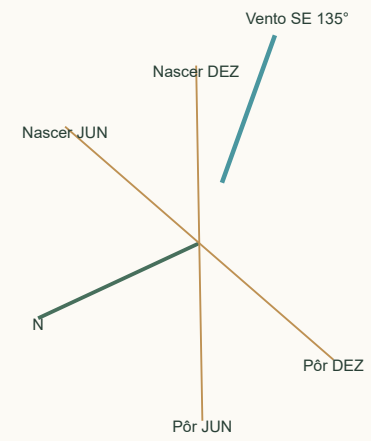

ESCALA GRÁFICA · metros



1:100 ao imprimir em A3, sem ajustar à folha.

Solo natural conservador: 127,23 m² (30,29%)

Inclui exclusão de vagas, piscina, pisos e beirais.


Estudo para avaliação. Executivo e licenças posteriores.

Cotas gerais nas faces externas; dimensões úteis estimadas no quadro.

PEDRINHAS · CASA DO ÁTRIO SOCIAL · PROJETO 04

IMPLANTAÇÃO E COBERTURA · CAIMENTOS PROPOSTOS

Estudo arquitetônico R1 · 13/11/2026 · dimensões em metros

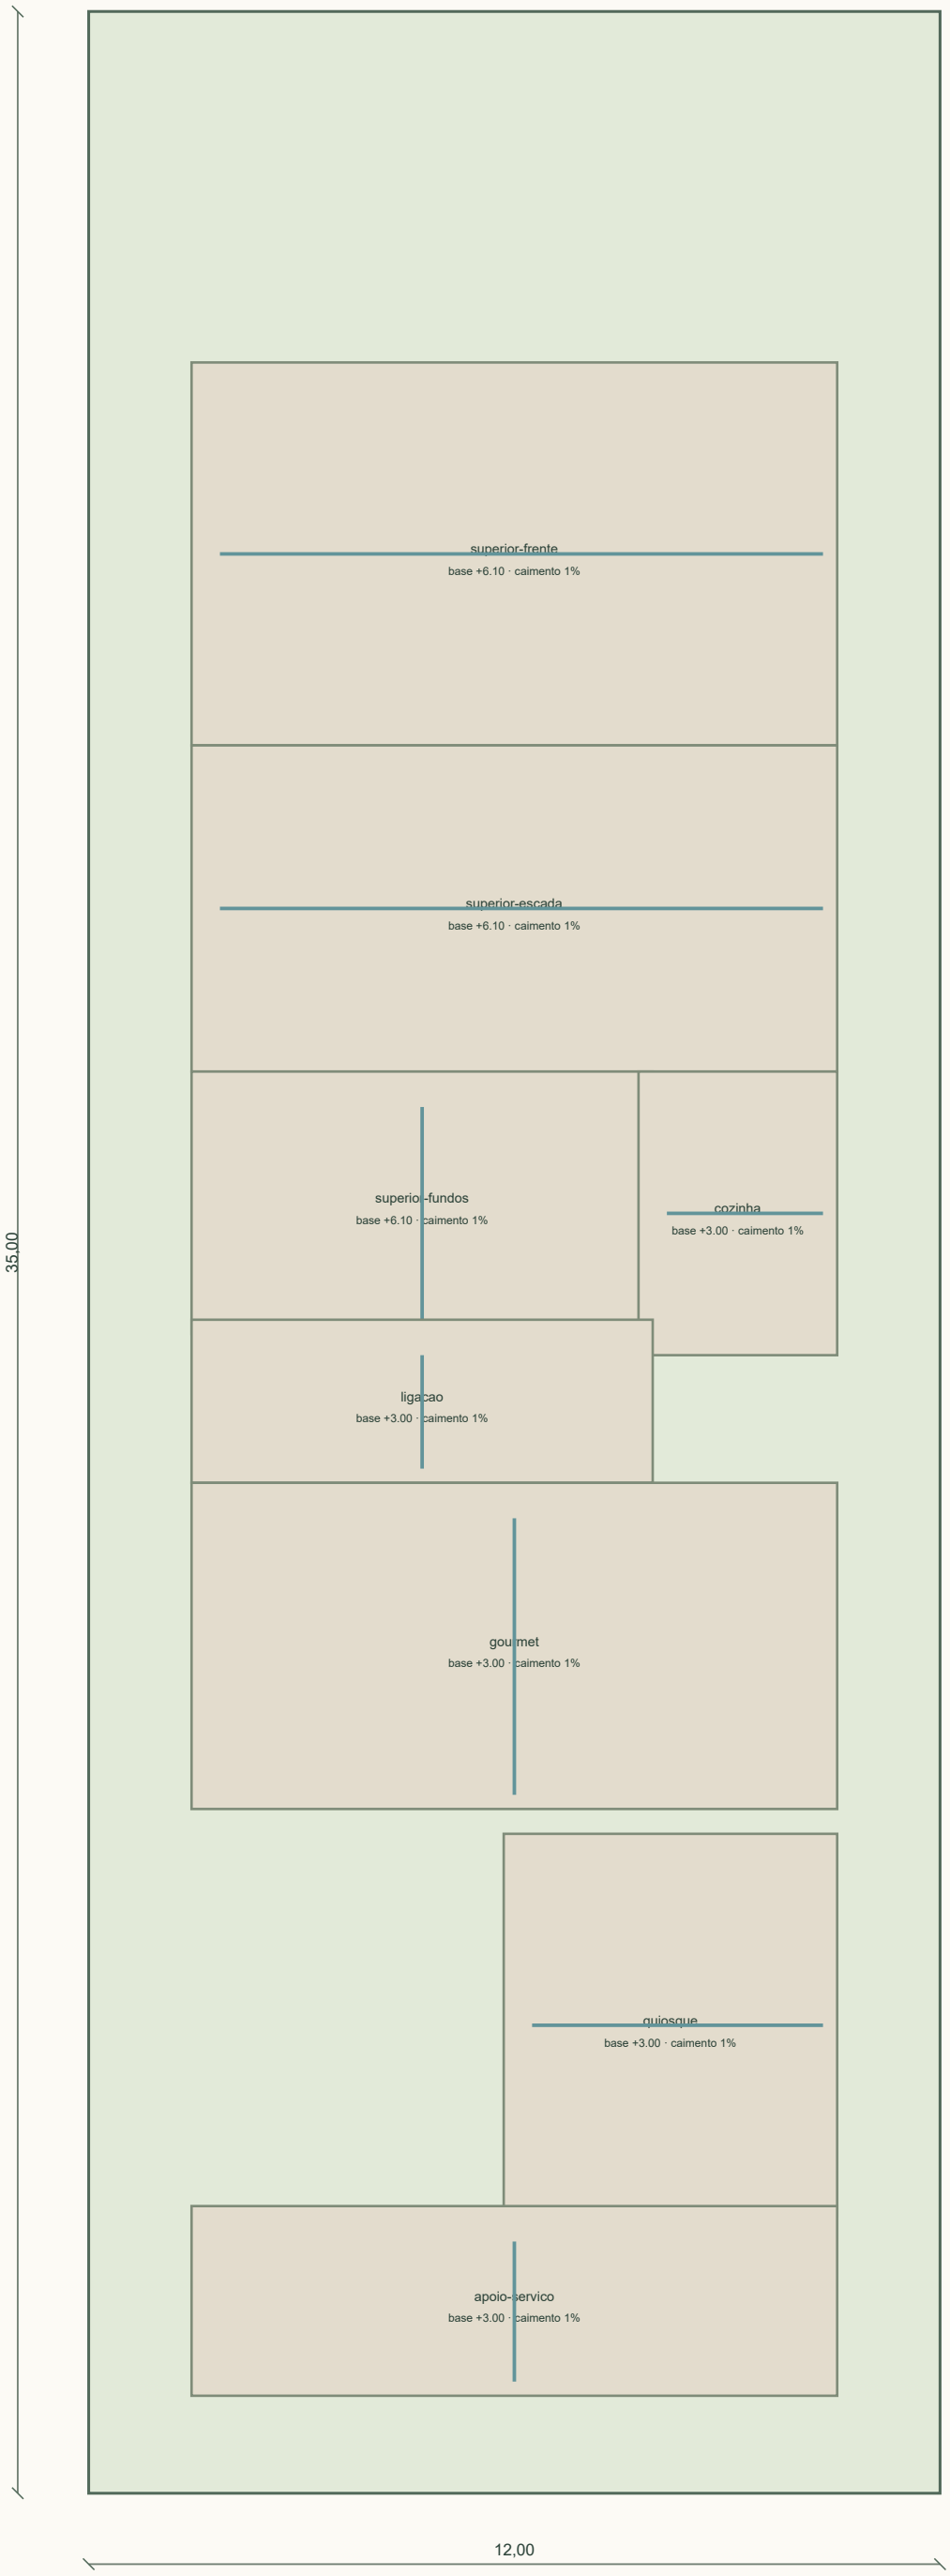

Lajes de cobertura com regularização inclinada.

Coletores e condutores representados no modelo.

Descarga prevista para sistema dentro do próprio lote.

Não usar muro do vizinho como apoio nem drenagem.

Pátio lateral aberto ao céu entre cozinha e gourmet.

Vão da escada coberto no nível superior, sem laje no vazio.

Cobertura da cozinha fechada nesta revisão.

Estrutura, impermeabilização e hidráulica: detalhar em executivo.

Recuos das faces de paredes/pilares:

Frente: mínimo desenhado 5,05 m

Laterais: mínimo desenhado 1,55 m

Fundos do bloco de apoio: 1,50 m

Beirais tratados separadamente; validação municipal necessária.

Não foi confirmada a zona cadastral do lote.


LC 034/2022: art. 141 remete ao Anexo 13-A.

A implantação atende às premissas do briefing;

isso não equivale a aprovação urbanística.

ESCADA EM U · CORTE DESENVOLVIDO ESQUEMÁTICO

Os dois lances aparecem desenvolvidos; não é um único plano de corte real.

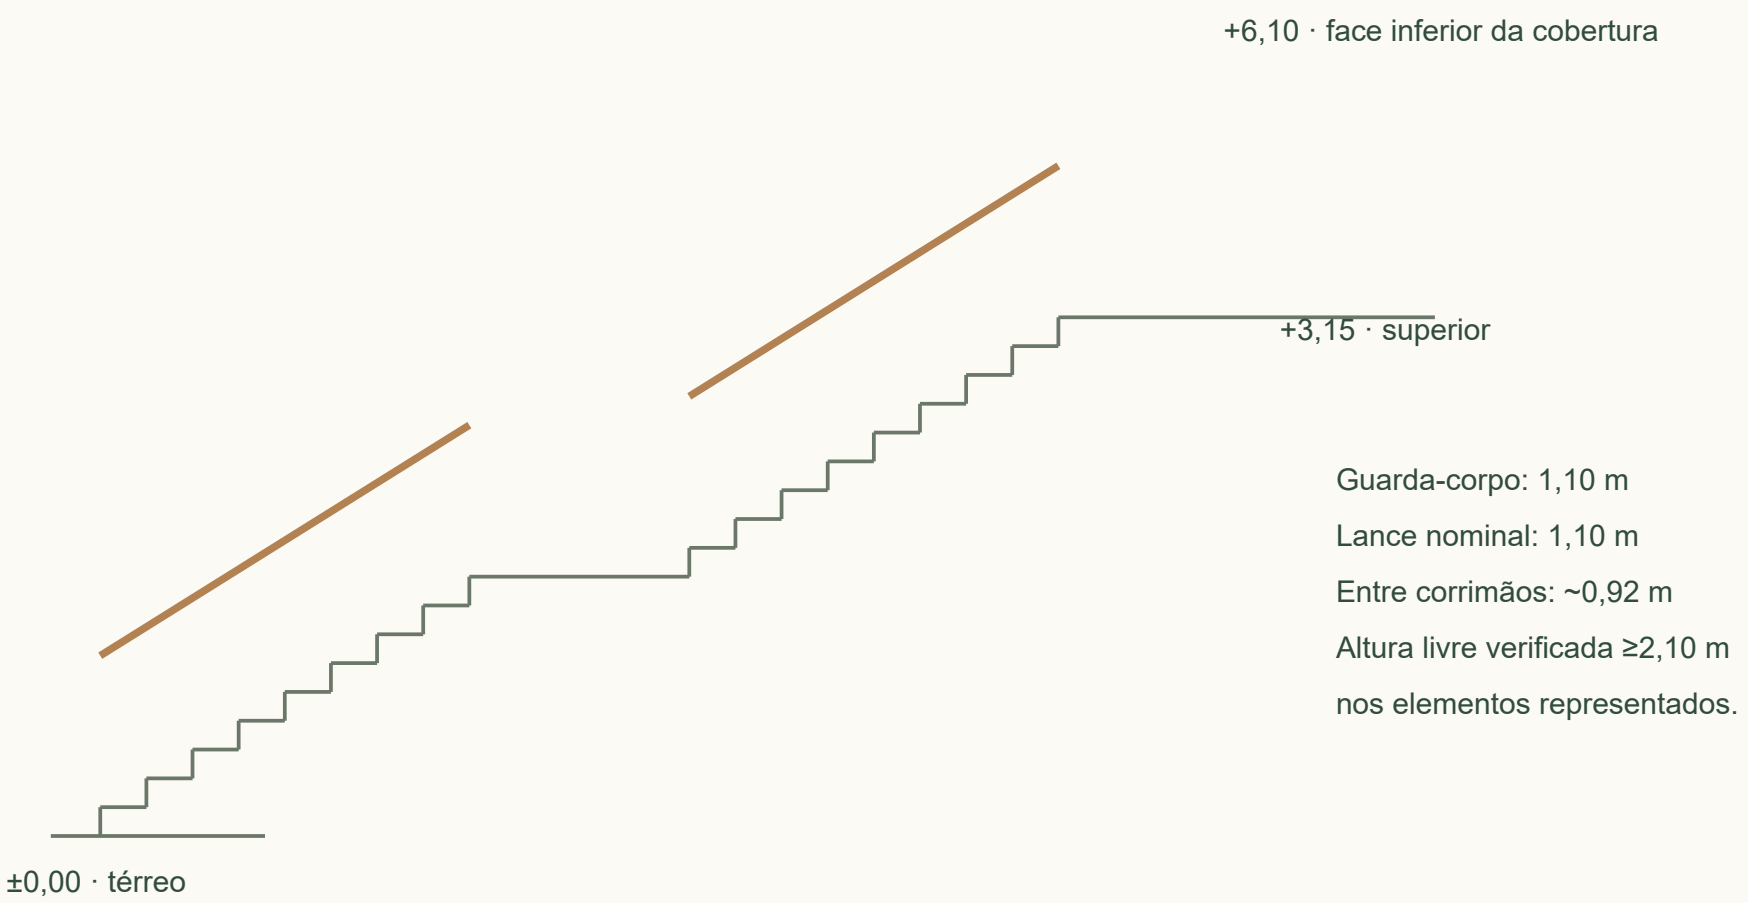

18 × 0,175 = 3,15 m · 16 pisos de 0,28 m + patamar · 2e+p = 0,63 m