PEDRINHAS / INGETRAZO

CASA 6 — Duas Varandas

TÉRREO · R2 / 13.11.2026 · ESTUDO PRELIMINAR



AMBIENTES E MEDIDAS ÚTEIS

Dimensões descontam 7,5 cm em cada face.

01 Quarto 1
3,55 × 3,65 m · 12,96 m²

02 Banho reversível 1
1,85 × 2,05 m · 3,79 m²

03 Vestíbulo 1
1,55 × 2,05 m · 3,18 m²

04 Quarto 2
3,55 × 3,65 m · 12,96 m²

05 Vestíbulo 2
1,55 × 2,05 m · 3,18 m²

06 Banho reversível 2
1,85 × 2,05 m · 3,79 m²

07 Galeria íntima
1,15 × 5,85 m · 6,73 m²

08 Entrada lateral / hall
2,65 × 1,05 m · 2,78 m²

09 Hall e jardim
2,05 × 5,85 m · 11,99 m²

10 Escada em U
2,65 × 3,44 m · 9,12 m²

11 Quarto 3
3,55 × 3,65 m · 12,96 m²

12 Vestíbulo 3
1,55 × 2,05 m · 3,18 m²

13 Banho reversível 3
1,85 × 2,05 m · 3,79 m²

14 Passeio coberto
2,05 × 1,35 m · 2,77 m²

15 Estar no jardim
4,85 × 3,80 m · 18,43 m²

16 Cozinha aberta
3,55 × 3,80 m · 13,49 m²

17 Varanda de refeições
8,55 × 3,55 m · 30,35 m²

18 Quiosque / estar
3,40 × 4,78 m · 16,23 m²

19 Lavanderia
2,25 × 2,05 m · 4,61 m²

20 Depósito
1,45 × 2,05 m · 2,97 m²

21 Lavabo piscina
1,85 × 2,05 m · 3,79 m²

22 Churrasqueira / apoio
2,55 × 2,05 m · 5,23 m²

Janelas maxim-ar ABREM PARA FORA.

Portas: giro em tracejado / correr em linha dupla.

Área de janela: conferir folha e ventilação efetiva.

Guarda-corpos 1,10 m; corrimãos nos dois lances.

Cotas são estudo, não dimensões de execução.

SOLO NATURAL: 129,42 m² (30,81%)

CONSTRUÍDA ESTIMADA: 321,60 m²


Recuos 5 / 1,5 / 1,5 m: hipótese do briefing.

Zona cadastral / condomínio: PENDENTES.

PEDRINHAS / INGETRAZO

CASA 6 — Duas Varandas

PAVIMENTO SUPERIOR · R2 / 13.11.2026 · ESTUDO PRELIMINAR

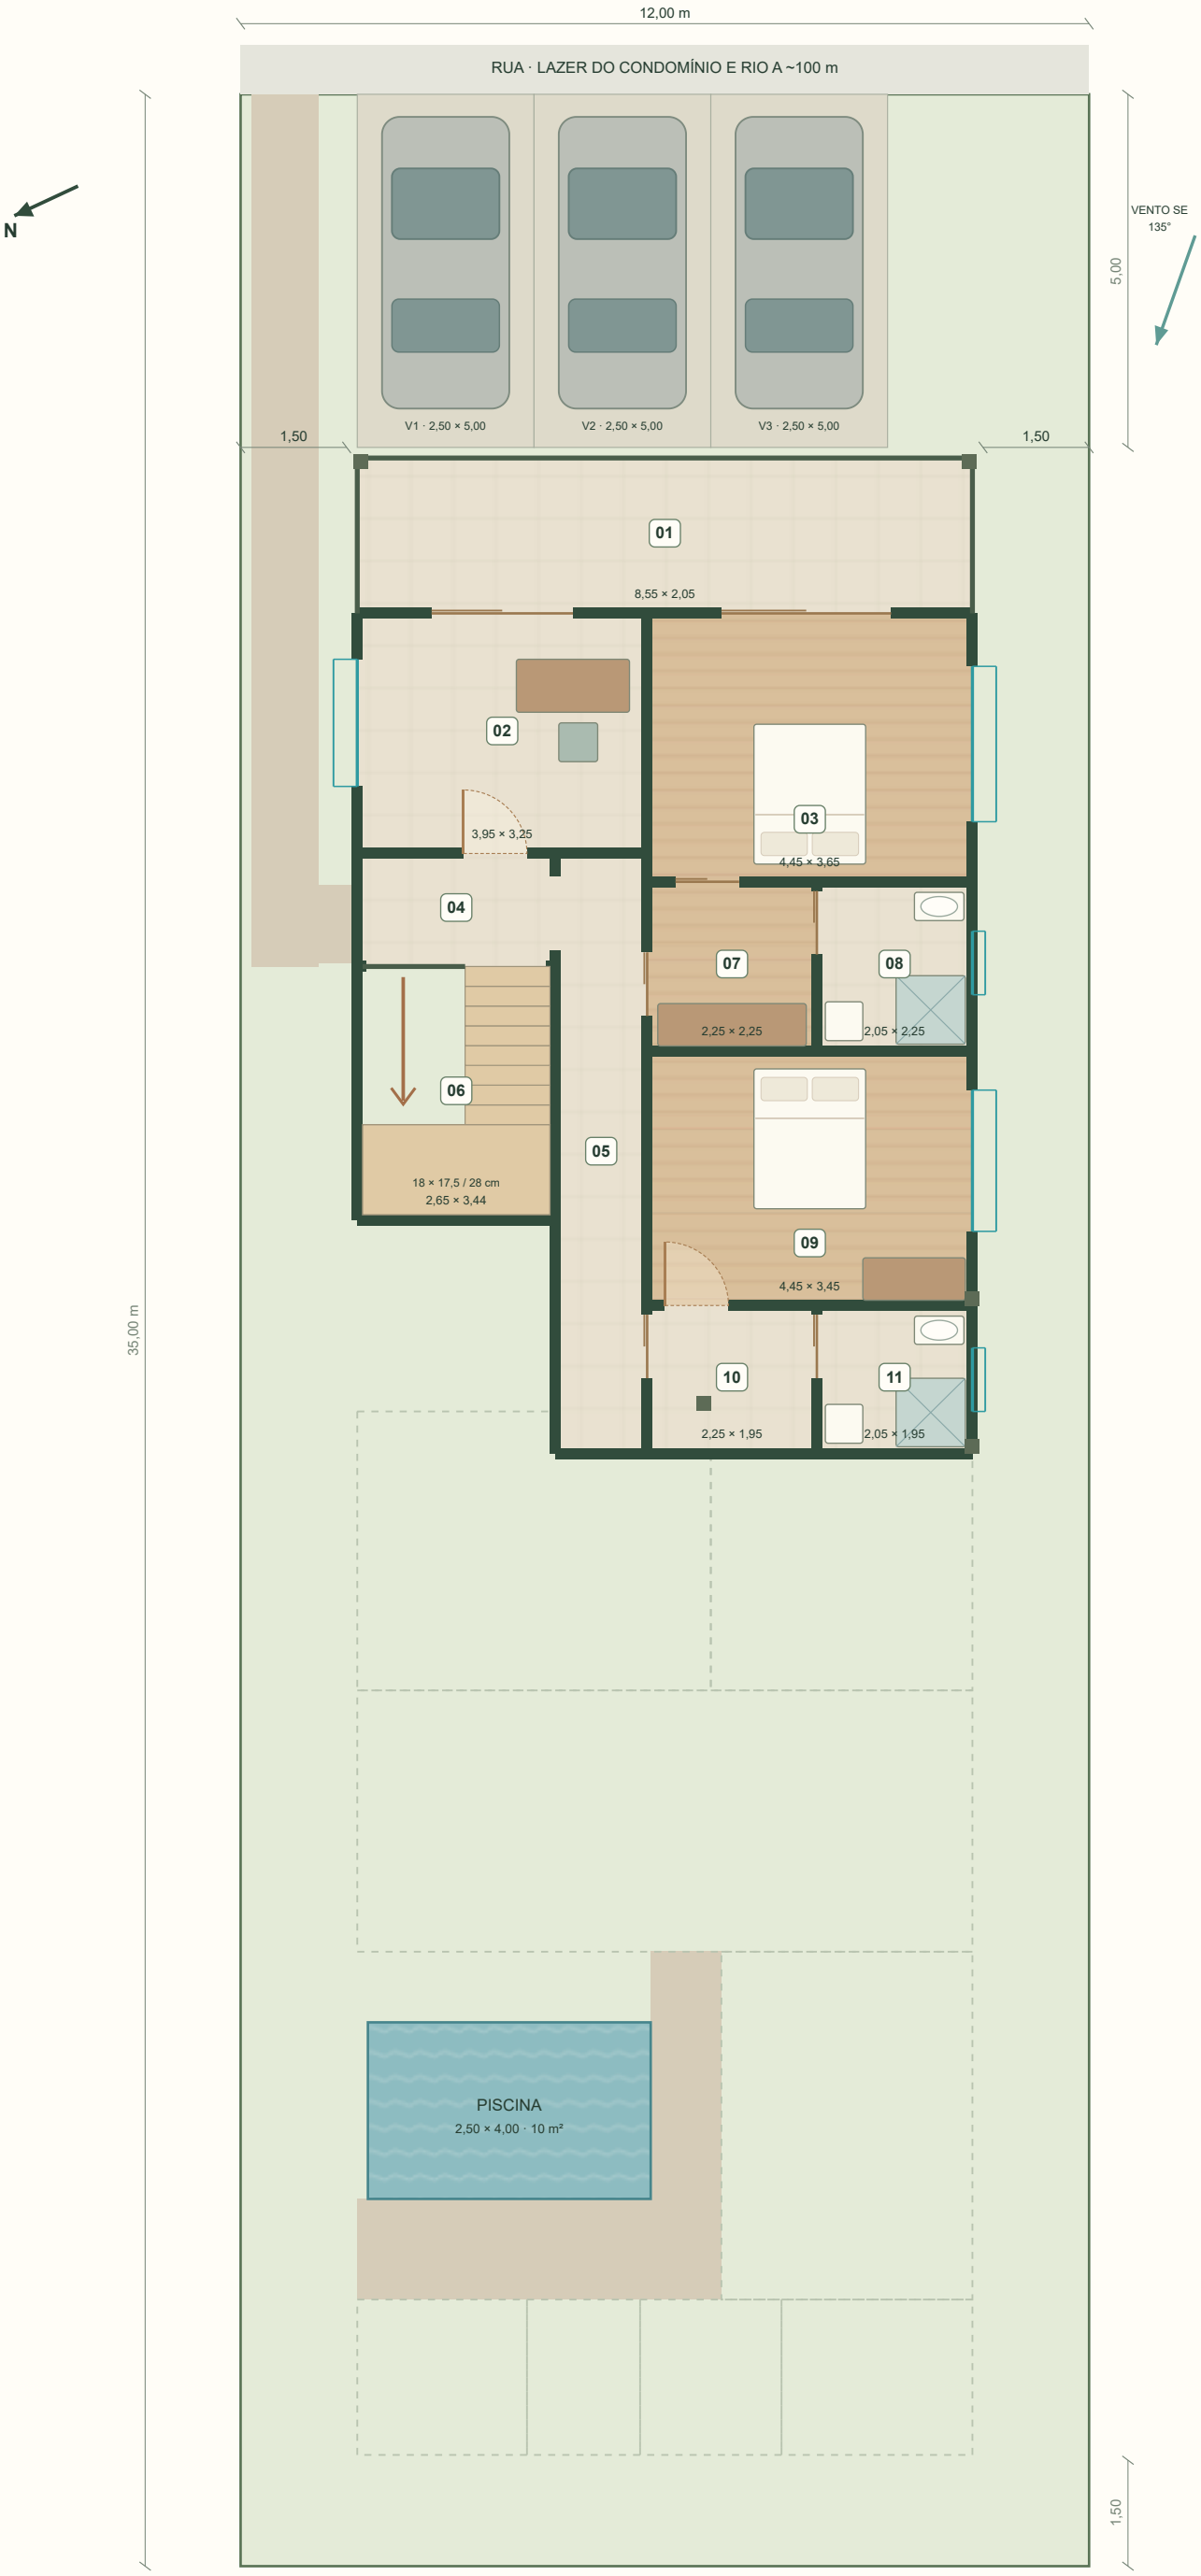

AMBIENTES E MEDIDAS ÚTEIS

Dimensões descontam 7,5 cm em cada face.

01 Varanda / rio
8,55 × 2,05 m · 17,53 m²

02 Escritório
3,95 × 3,25 m · 12,84 m²

03 Suíte master
4,45 × 3,65 m · 16,24 m²

04 Chegada da escada
2,65 × 1,45 m · 3,84 m²

05 Galeria superior
1,15 × 8,35 m · 9,60 m²

06 Vazio protegido
2,65 × 3,44 m · 9,12 m²

07 Closet / acesso master
2,25 × 2,25 m · 5,06 m²

08 Banho master
2,05 × 2,25 m · 4,61 m²

09 Suíte 5
4,45 × 3,45 m · 15,35 m²

10 Vestíbulo suíte 5
2,25 × 1,95 m · 4,39 m²

11 Banho suíte 5
2,05 × 1,95 m · 4,00 m²

Janelas maxim-ar ABREM PARA FORA.

Portas: giro em tracejado / correr em linha dupla.

Área de janela: conferir folha e ventilação efetiva.

Guarda-corpos 1,10 m; corrimãos nos dois lances.

Cotas são estudo, não dimensões de execução.

SOLO NATURAL: 129,42 m² (30,81%)

CONSTRUÍDA ESTIMADA: 321,60 m²

Recuos 5 / 1,5 / 1,5 m: hipótese do briefing.

Zona cadastral / condomínio: PENDENTES.